

отметка чистого пола +0.150, в разрезе +0.250. надземных этажей 17, в задании 16.

ЭКСПЛИКАЦИЯ

площадь застройки принята 2450 м2, по расчёту ПЗУ 2180 м2

площадь квартиры 105 равна 38.4 м2, по обмеру 42.1 м2

лифт 1000 кг, по заданию 630 кг

ширина лестничного марша принята 1.20 м, по нормам 1.35 м

N




ПЛАН ТИПОВОГО ЭТАЖА (2–16). Секции 1–3

отметка чистого пола +0.150, в разрезе +0.250. надземных этажей 17, в задании 16.

ЭКСПЛИКАЦИЯ
площадь застройки принята 2450 м2, по расчёту ПЗУ 2180 м2
площадь квартиры 105 равна 38.4 м2, по обмеру 42.1 м2
лифт 1000 кг, по заданию 630 кг
ширина лестничного марша принята 1.20 м, по нормам 1.35 м

N
|

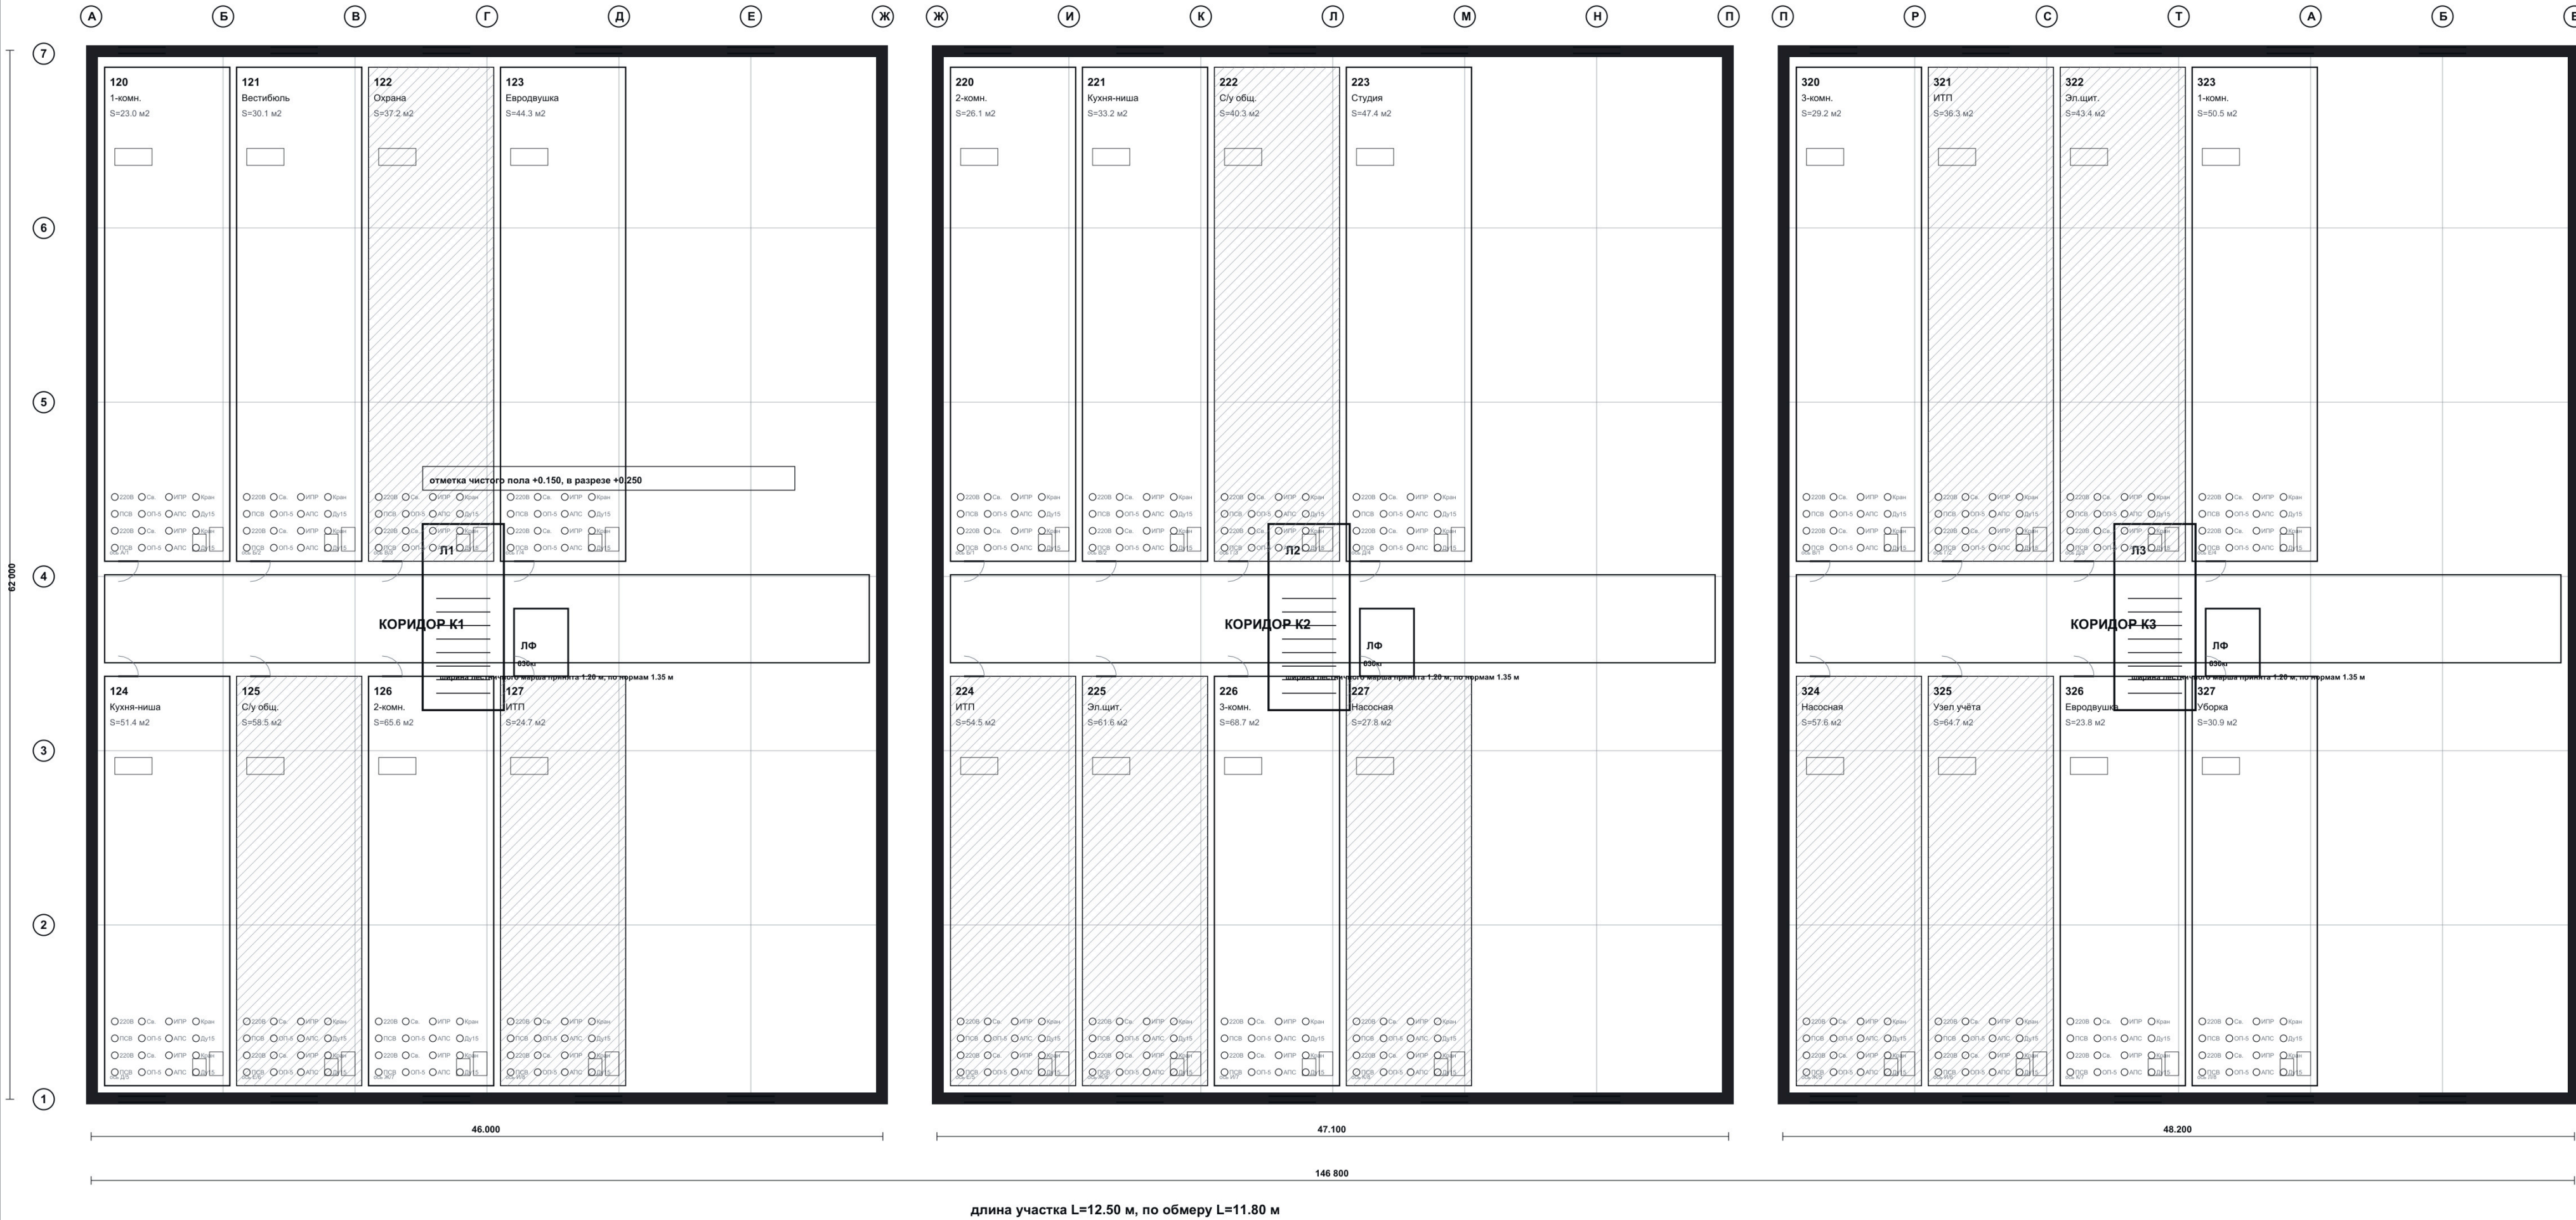

Объект Северный квартал	Лист 2/8	Стадия П
ПЛАН ТИПОВОГО ЭТАЖА (2–16). Секции		
		АР-ПЗУ

ГЕНПЛАН. Схема планировочной организации земельного участка


площадь застройки принята 2450 м2, по расчёту ПЗУ 2180 м2. озеленение участка 28 %, по ПЗЗ не менее 35 %. машиномест в стилобате 86, по расчёту требуется 72.



Объект	Лист	Стадия
Северный квартал	5/8	П
Генплан ПЗУ		
		АР-ПЗУ

РАЗРЕЗ 1–1. По лестничной клетке Л1


высота здания 54.00 м, по разрезу 51.60 м, надземных этажей 17, в задании 16.

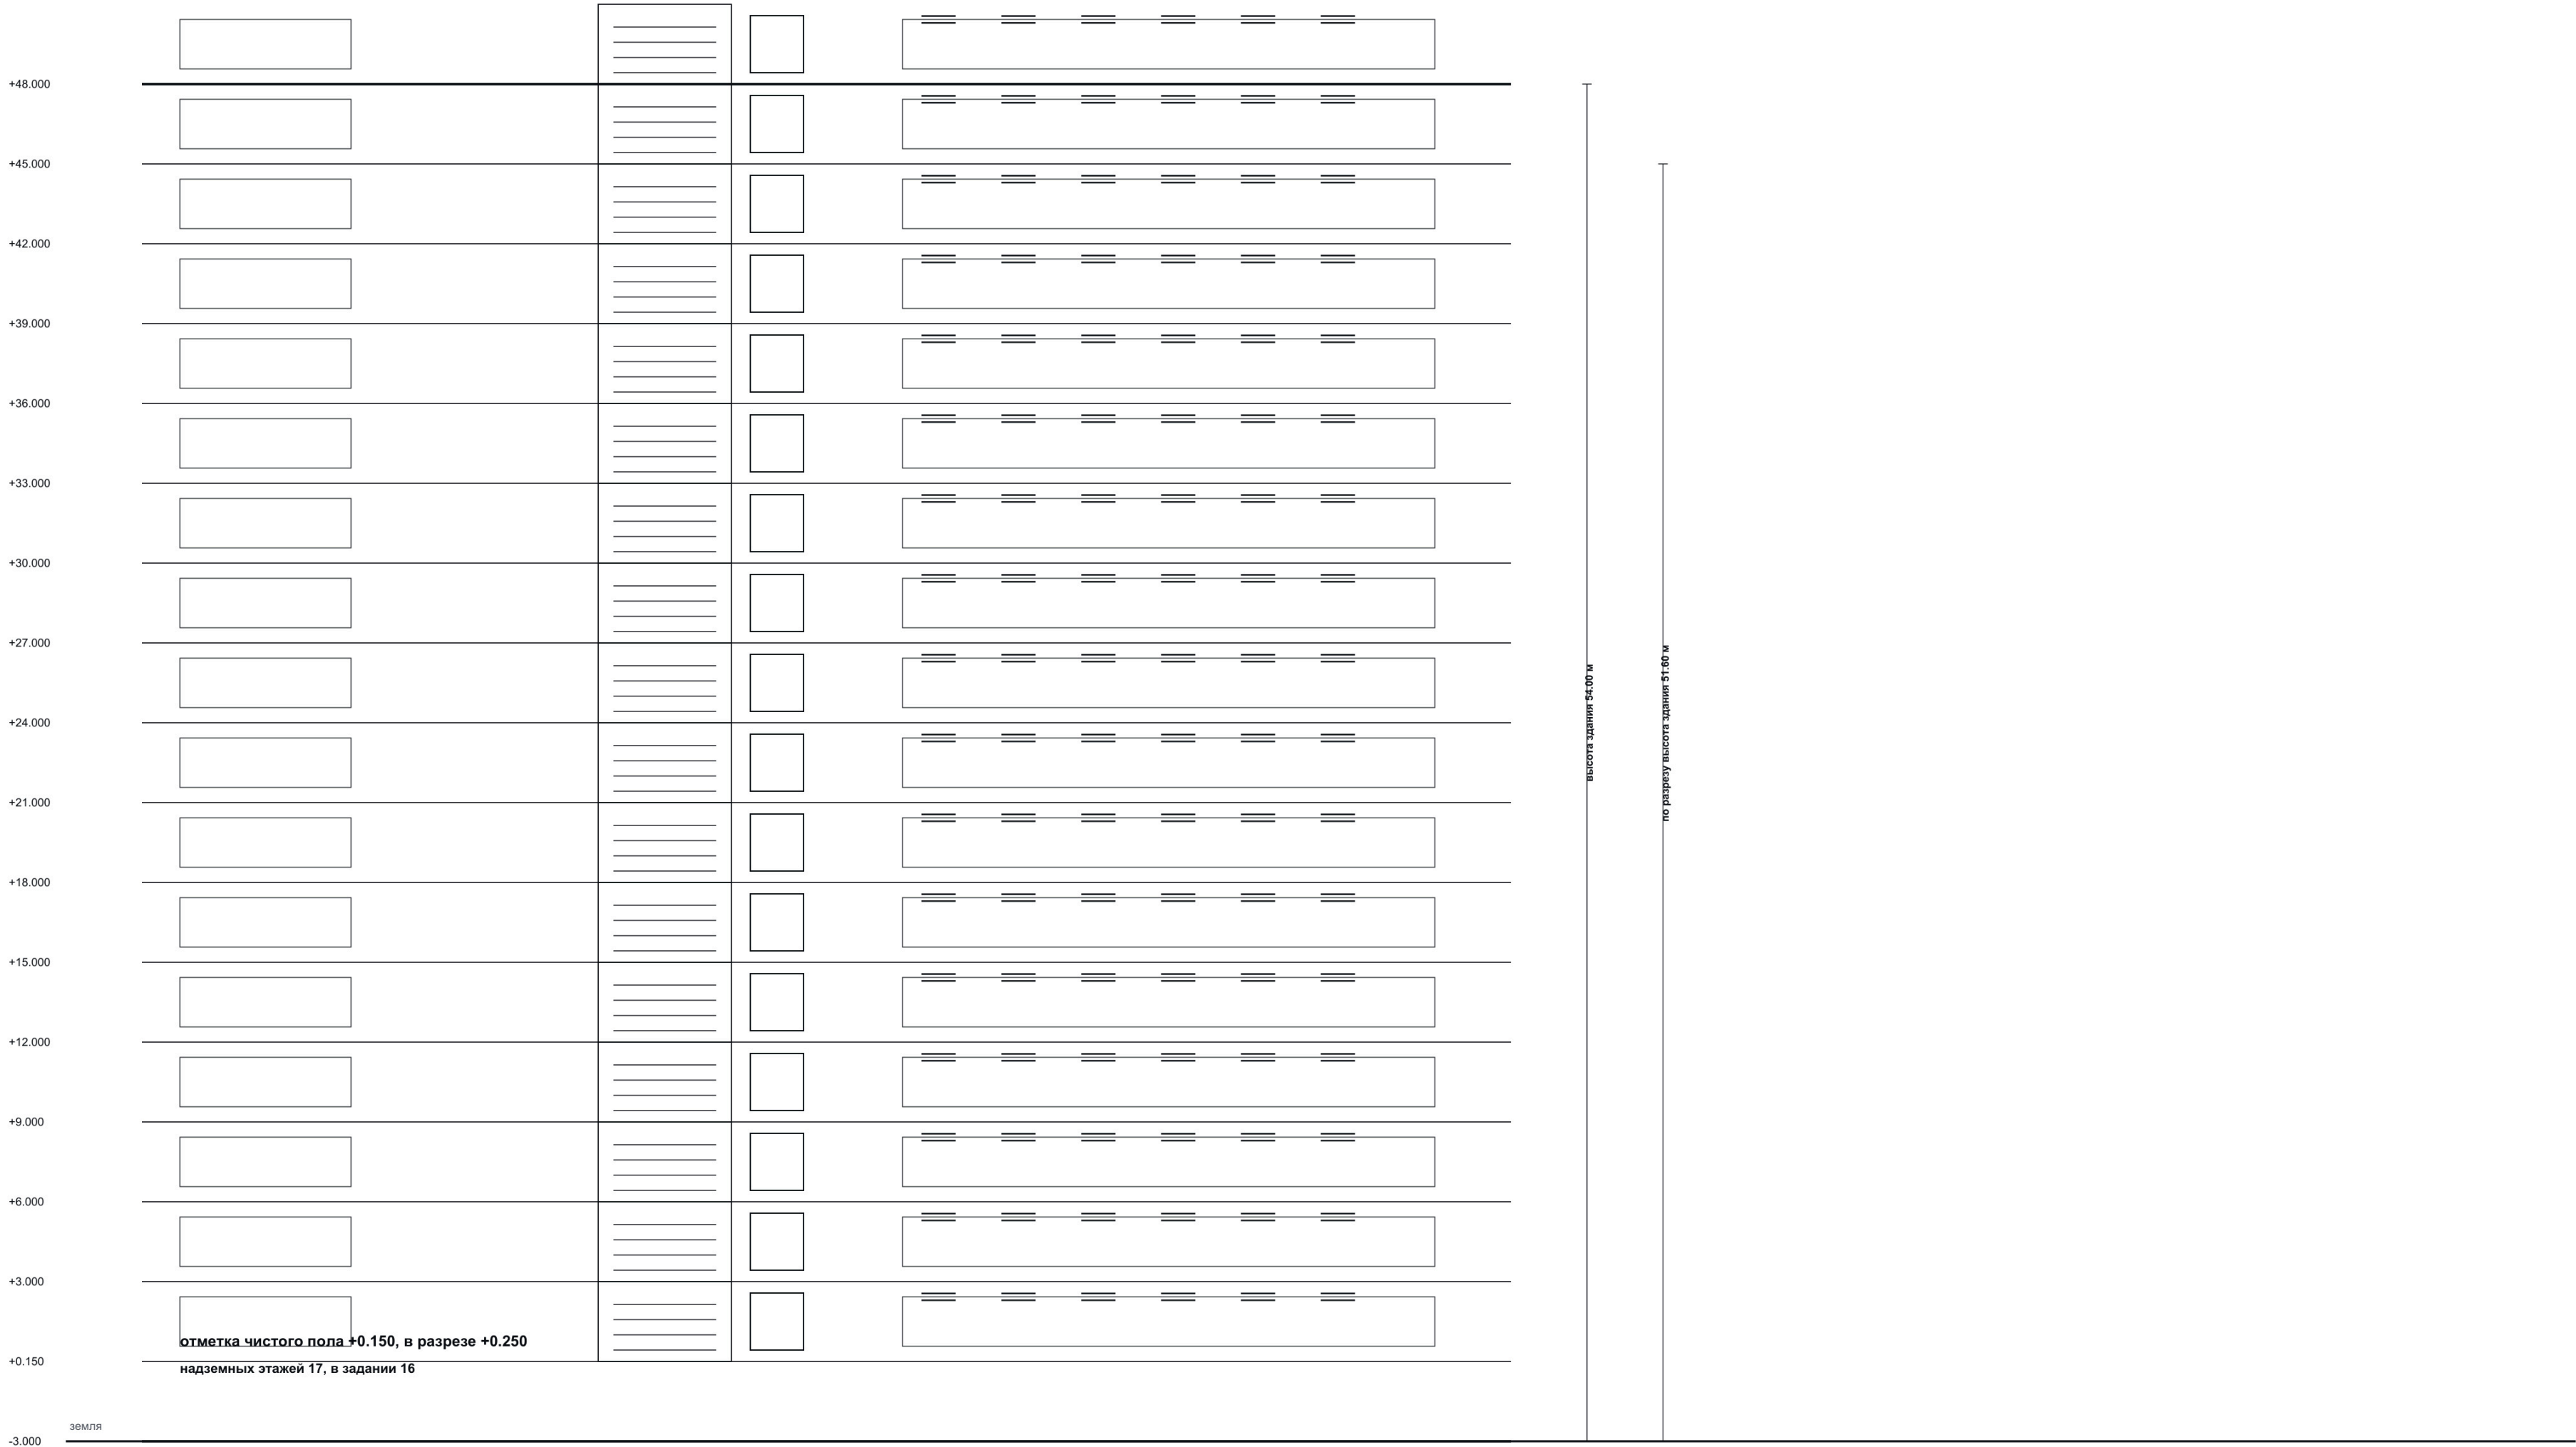

Объект Северный квартал	Лист 6/8	Стадия П
Разрез 1-1		
		АР-ПЗУ

ФАСАД 1–3. Со стороны внутриквартального проезда

высота здания 54.00 м, по разрезу 51.60 м. степень огнестойкости принята II, в задании III.

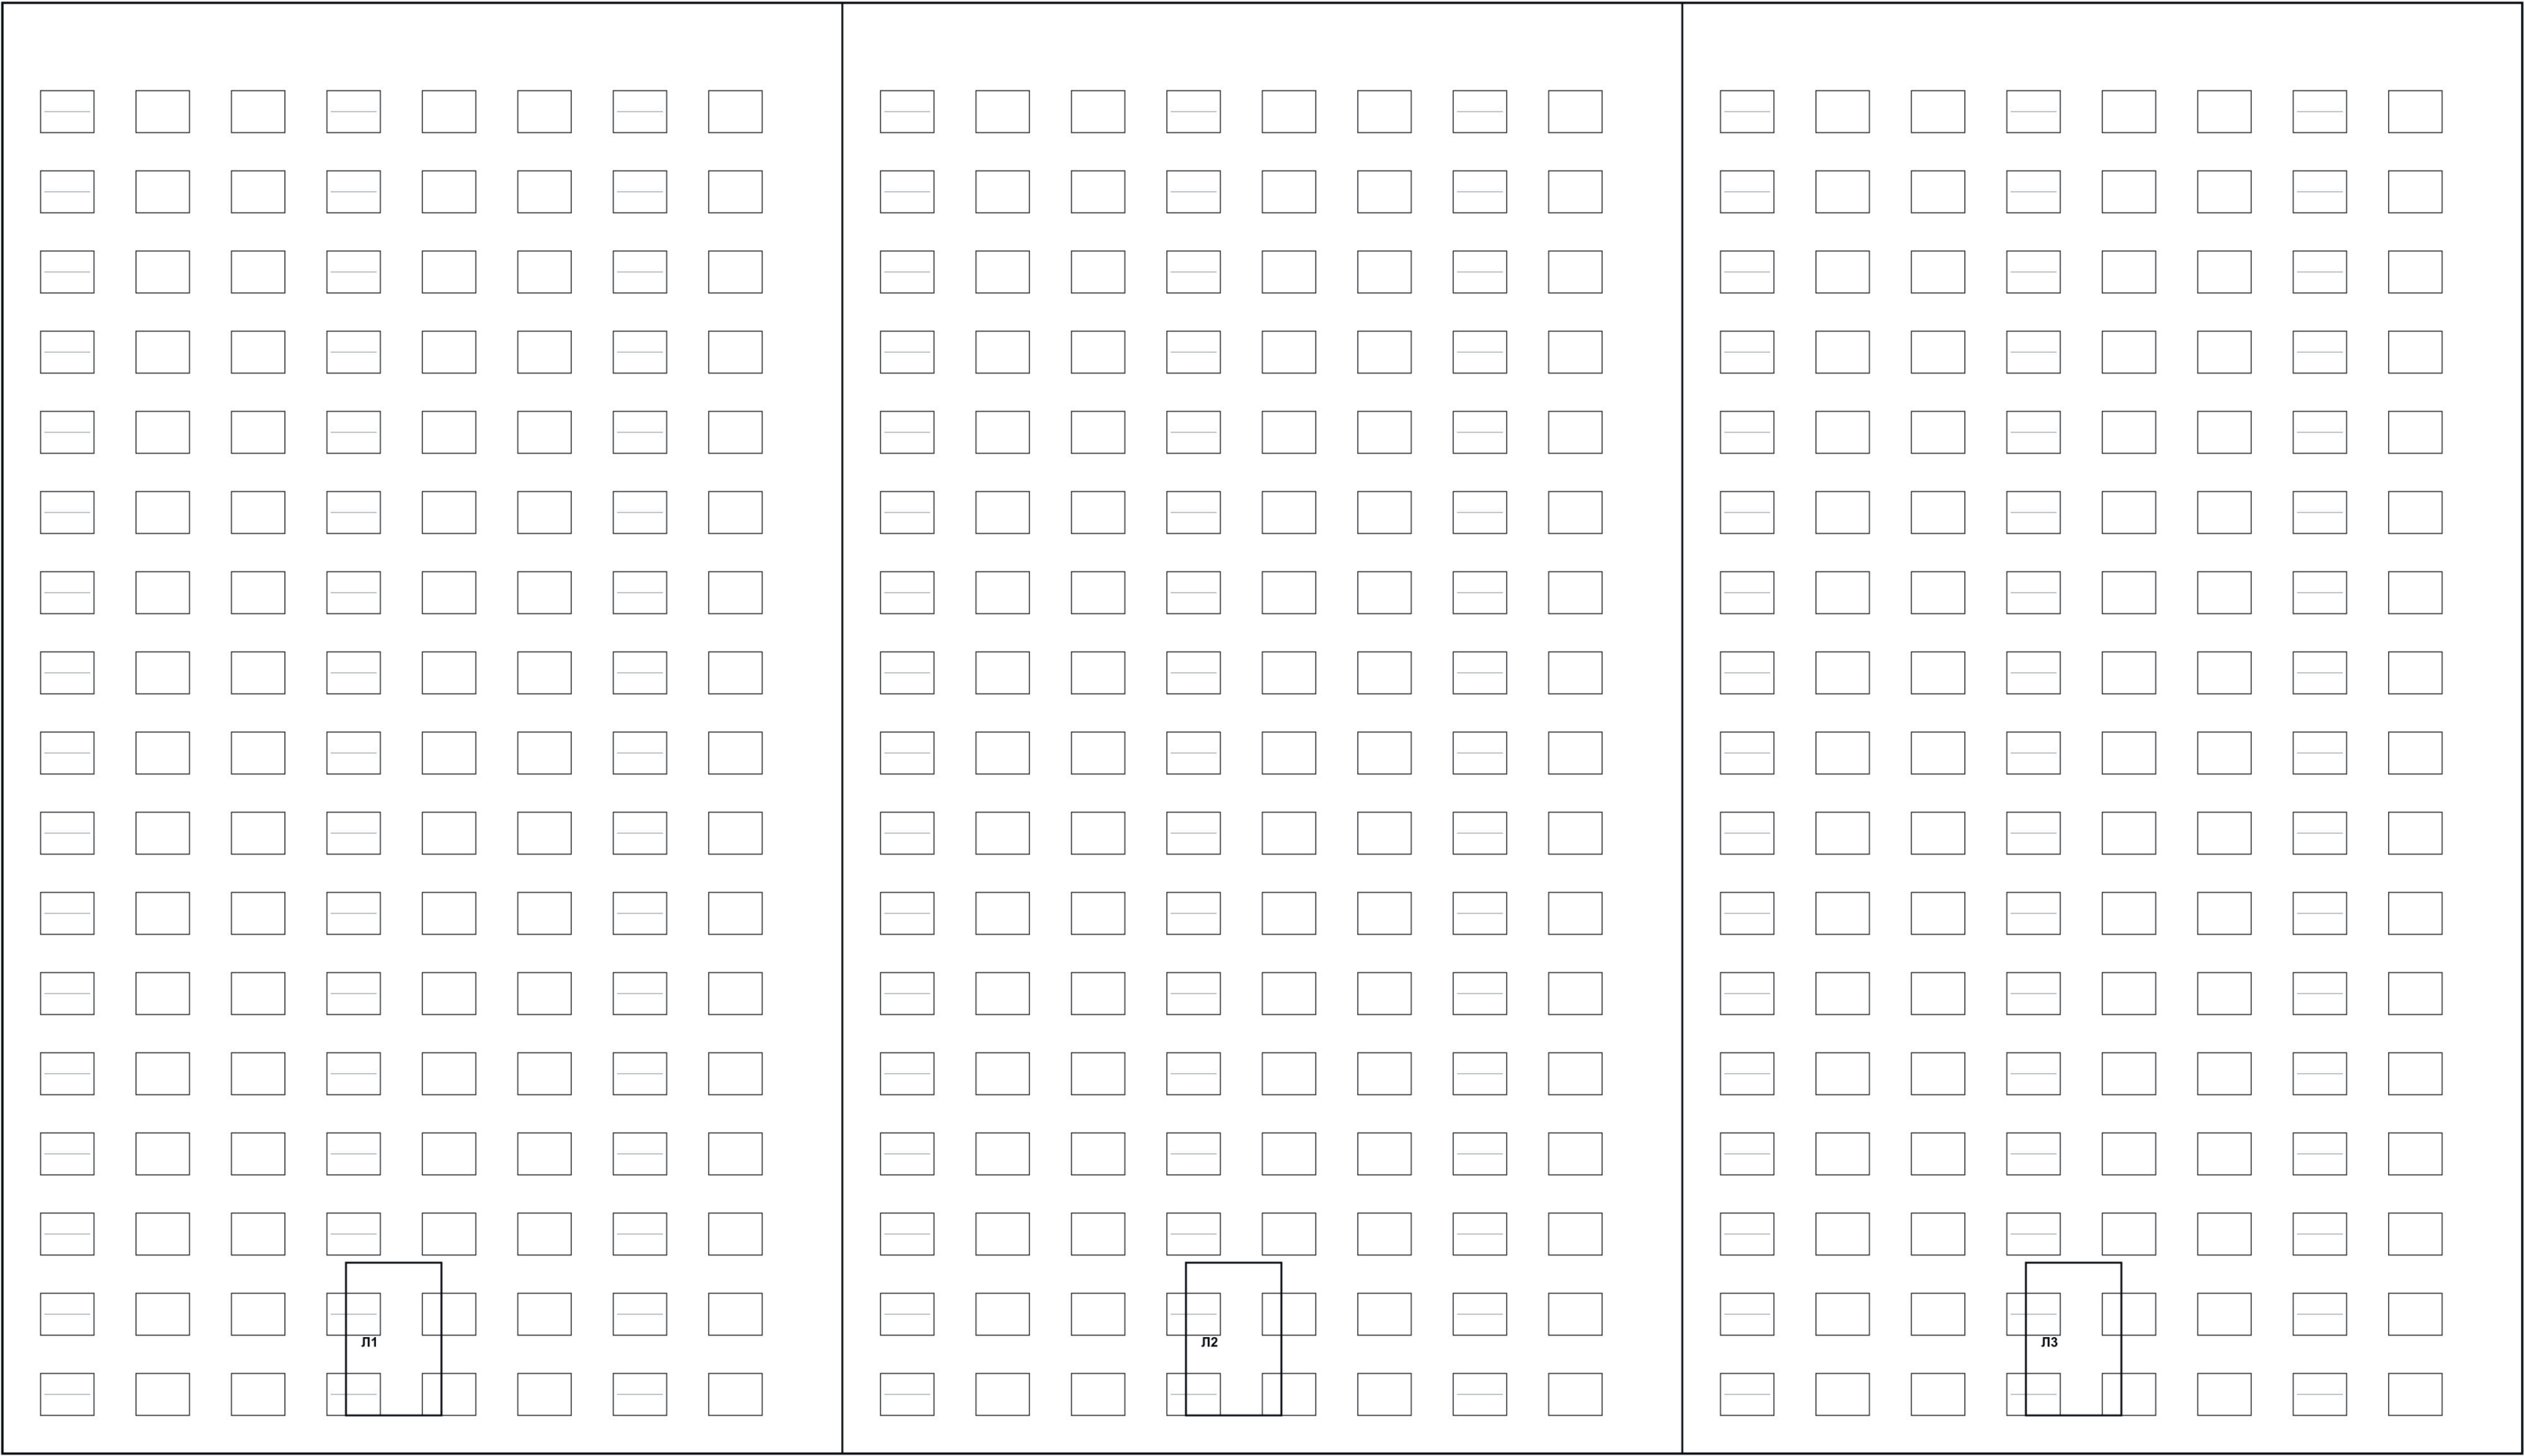

высота здания 54.00 м, по разрезу 51.60 м

Объект Северный квартал	Лист 7/8	Стадия П
Фасад 1-3		
		АР-ПЗУ

ПЛАН СТИЛОБАТА. Парковка и пожарные проезды

1201	1202	1203	1204	1205	1206	1207	1208	1209	1210	1211	1212	1213	1214	1215	1216	1217	1218	1219	1220	1221	1222
1101	1102	1103	1104	1105	1106	1107	1108	1109	1110	1111	1112	1113	1114	1115	1116	1117	1118	1119	1120	1121	1122
1001	1002	1003	1004	1005	1006	1007	1008	1009	1010	1011	1012	1013	1014	1015	1016	1017	1018	1019	1020	1021	1022
901	902	903	904	905	906	907	908	909	910	911	912	913	914	915	916	917	918	919	920	921	922
801	802	803	804	805	806	807	808	809	810	811	812	813	814	815	816	817	818	819	820	821	822
701	702	703	704	705	706	707	708	709	710	711	712	713	714	715	716	717	718	719	720	721	722
601	602	603	604	605	606	607	608	609	610	611	612	613	614	615	616	617	618	619	620	621	622
501	502	503	504	505	506	507	508	509	510	511	512	513	514	515	516	517	518	519	520	521	522
401	402	403	404	405	406	407	408	409	410	411	412	413	414	415	416	417	418	419	420	421	422
301	302	303	304	305	306	307	308	309	310	311	312	313	314	315	316	317	318	319	320	321	322
201	202	203	204	205	206	207	208	209	210	211	212	213	214	215	216	217	218	219	220	221	222
101	102	103	104	105	106	107	108	109	110	111	112	113	114	115	116	117	118	119	120	121	122

машиномест в стилобате 86, по расчёту требуется 72


УЗЕЛ УЧЁТА ВОДЫ. Обязка ИТП

поз.127  ПСВ-10	поз.128  ОП-5-10	поз.129  АПС-10	поз.130  Ду15-10	поз.131  220B-10	поз.132  Св.-10	поз.133  ИПР-10	поз.134  Кран-10	поз.135  ПСВ-10	поз.136  ОП-5-10	поз.137  АПС-10	поз.138  Ду15-10	поз.139  220B-10	поз.140  Св.-10
поз.113  ПСВ-9	поз.114  ОП-5-9	поз.115  АПС-9	поз.116  Ду15-9	поз.117  220B-9	поз.118  Св.-9	поз.119  ИПР-9	поз.120  Кран-9	поз.121  ПСВ-9	поз.122  ОП-5-9	поз.123  АПС-9	поз.124  Ду15-9	поз.125  220B-9	поз.126  Св.-9
поз.99  ПСВ-8	поз.100  ОП-5-8	поз.101  АПС-8	поз.102  Ду15-8	поз.103  220B-8	поз.104  Св.-8	поз.105  ИПР-8	поз.106  Кран-8	поз.107  ПСВ-8	поз.108  ОП-5-8	поз.109  АПС-8	поз.110  Ду15-8	поз.111  220B-8	поз.112  Св.-8
поз.85  ПСВ-7	поз.86  ОП-5-7	поз.87  АПС-7	поз.88  Ду15-7	поз.89  220B-7	поз.90  Св.-7	поз.91  ИПР-7	поз.92  Кран-7	поз.93  ПСВ-7	поз.94  ОП-5-7	поз.95  АПС-7	поз.96  Ду15-7	поз.97  220B-7	поз.98  Св.-7
поз.71  ПСВ-6	поз.72  ОП-5-6	поз.73  АПС-6 по ТУ ввод водопровода Ду80	поз.74  Ду15-6	поз.75  220B-6	поз.76  Св.-6	поз.77  ИПР-6	поз.78  Кран-6	поз.79  ПСВ-6	поз.80  ОП-5-6	поз.81  АПС-6	поз.82  Ду15-6	поз.83  220B-6	поз.84  Св.-6
поз.57  ПСВ-5	поз.58  ОП-5-5	поз.59  АПС-5 ввод водопровода Ду100	поз.60  Ду15-5	поз.61  220B-5	поз.62  Св.-5	поз.63  ИПР-5	поз.64  Кран-5	поз.65  ПСВ-5	поз.66  ОП-5-5	поз.67  АПС-5	поз.68  Ду15-5	поз.69  220B-5	поз.70  Св.-5
поз.43  ПСВ-4	поз.44  ОП-5-4 по заданию требуется 4 шт ВСХН-20	поз.45  АПС-4	поз.46  Ду15-4	поз.47  220B-4	поз.48  Св.-4	поз.49  ИПР-4	поз.50  Кран-4	поз.51  ПСВ-4	поз.52  ОП-5-4	поз.53  АПС-4	поз.54  Ду15-4	поз.55  220B-4	поз.56  Св.-4
поз.29  ПСВ-3	поз.30  ОП-5-3 7 шт счетчик ВСХН-20 количество 7 шт	поз.31  АПС-3	поз.32  Ду15-3	поз.33  220B-3	поз.34  Св.-3	поз.35  ИПР-3	поз.36  Кран-3	поз.37  ПСВ-3	поз.38  ОП-5-3	поз.39  АПС-3	поз.40  Ду15-3	поз.41  220B-3	поз.42  Св.-3
поз.15  ПСВ-2	поз.16  ОП-5-2	поз.17  АПС-2	поз.18  Ду15-2	поз.19  220B-2	поз.20  Св.-2	поз.21  ИПР-2	поз.22  Кран-2	поз.23  ПСВ-2	поз.24  ОП-5-2	поз.25  АПС-2	поз.26  Ду15-2	поз.27  220B-2	поз.28  Св.-2
поз.1  ПСВ-1	поз.2  ОП-5-1	поз.3  АПС-1	поз.4  Ду15-1	поз.5  220B-1	поз.6  Св.-1	поз.7  ИПР-1	поз.8  Кран-1	поз.9  ПСВ-1	поз.10  ОП-5-1	поз.11  АПС-1	поз.12  Ду15-1	поз.13  220B-1	поз.14  Св.-1

ТЕХНИКО-ЭКОНОМИЧЕСКИЕ ПОКАЗАТЕЛИ. Сложная ведомость

Объединённые ячейки, цветные строки. Сверять с чертежами 1–7.

ТЕХНИКО-ЭКОНОМИЧЕСКИЕ ПОКАЗАТЕЛИ И ВЕДОМОСТЬ				
Поз	Наименование	По проекту	По заданию	Пом.
1. Площади и объёмы				
1	площадь застройки принята 2450 м2, по расчёту ПЗУ 2180 м2	2450	2180	ПЗУ
2	высота здания 54.00 м, по разрезу 51.60 м	54.00	51.60	фасад
2. Инженерное оборудование				
3	счетчик ВСХН-20: принято 7 шт, по заданию 4 шт	7	4	ошибка
4 ввод водопровода принят Ду100, по ТУ Ду80				
5	лифт 1000 кг, по заданию 630 кг	1000	630	Л1
3. Техничко-экономические показатели				
6	надземных этажей 17, в задании 16	17	16	ПЗ
7	озеленение участка 28 %, по ПЗЗ не менее 35 %	28	35	норма
8	расчётная мощность 250 кВт, по ТУ 180 кВт	250	180	ЭОМ
9	машиномест в стилобате 86, по расчёту требуется 72	86	72	ПЗУ
10	степень огнестойкости принята II, в задании III	II	III	ПЗ
итого единиц оборудования 18 шт, сумма строк 12				
4. Справочные показатели (без расхождений, шум для модели)				
11	Площадь участка, м2	8640	8640	ПЗУ
12	Строительный объём, м3	41200	41200	АР
13	Жилая площадь, м2	9860	9860	АР
14	Общая площадь квартир, м2	12440	12440	АР
15	Число квартир	216	216	ПЗ
16	Детская площадка, м2	180	180	ПЗУ
17	Спортплощадка, м2	240	240	ПЗУ
18	Контейнерная, м2	36	36	ПЗУ
19	Нагрузка на покрытие, кПа	2.4	2.4	КР
20	Снеговой район	III	III	КР

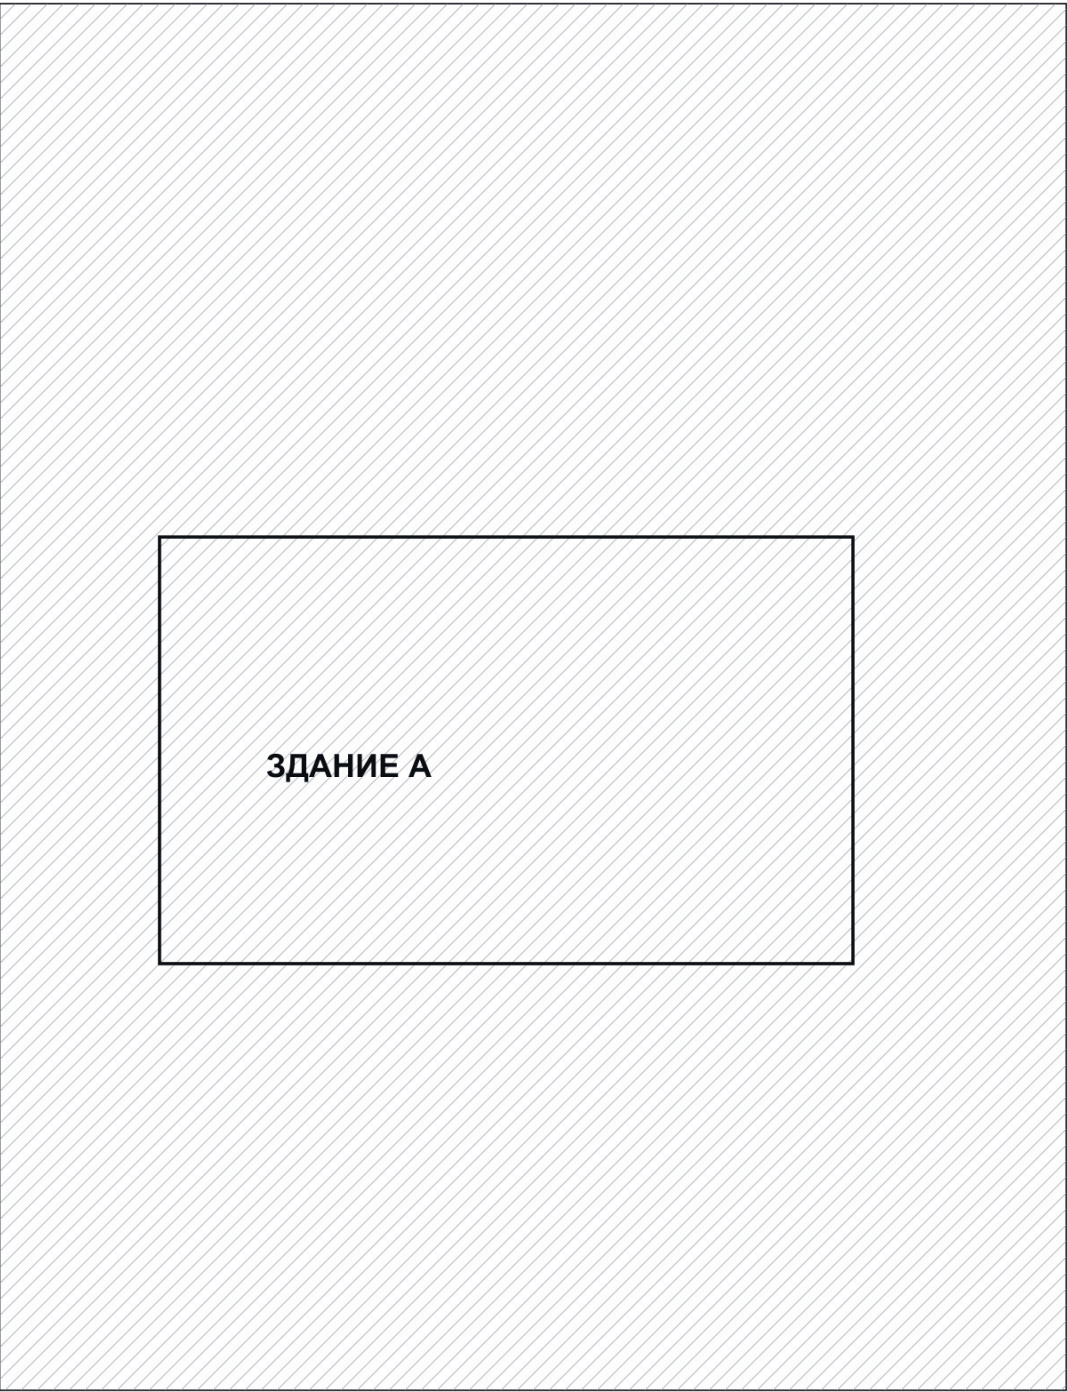

ввод водопровода Ду80

ввод водопровода Ду100

Сводка показателей листа

- 1. площадь застройки принята 2450 м2, по расчёту ПЗУ 2180 м2.
- 2. масштаб чертежа 1:100, в задании указан масштаб 1:200.
- 3. длина участка L=12.50 м, по обмеру L=11.80 м.
- 4. счетчик ВСХН-20: принято 7 шт, по заданию 4 шт.
- 5. отметка чистого пола +0.150, в разрезе +0.250.
- 6. высота здания 54.00 м, по разрезу 51.60 м.
- 7. машиномест в стилобате 86, по расчёту требуется 72.
- 8. степень огнестойкости принята II, в задании III.
- 9. лифт 1000 кг, по заданию 630 кг.
- 10. ввод водопровода принят Ду100, по ТУ Ду80.
- 11. надземных этажей 17, в задании 16.
- 12. озеленение участка 28 %, по ПЗЗ не менее 35 %.
- 13. площадь квартиры 105 равна 38.4 м2, по обмеру 42.1 м2.
- 14. ширина лестничного марша принята 1.20 м, по нормам 1.35 м.
- 15. расчётная мощность 250 кВт, по ТУ 180 кВт.
- 16. итого единиц оборудования 18 шт, сумма строк 12.

Объект Северный квартал	Лист 8/8	Стадия П
ТЭП и ведомость		
		АР-ПЗУ