


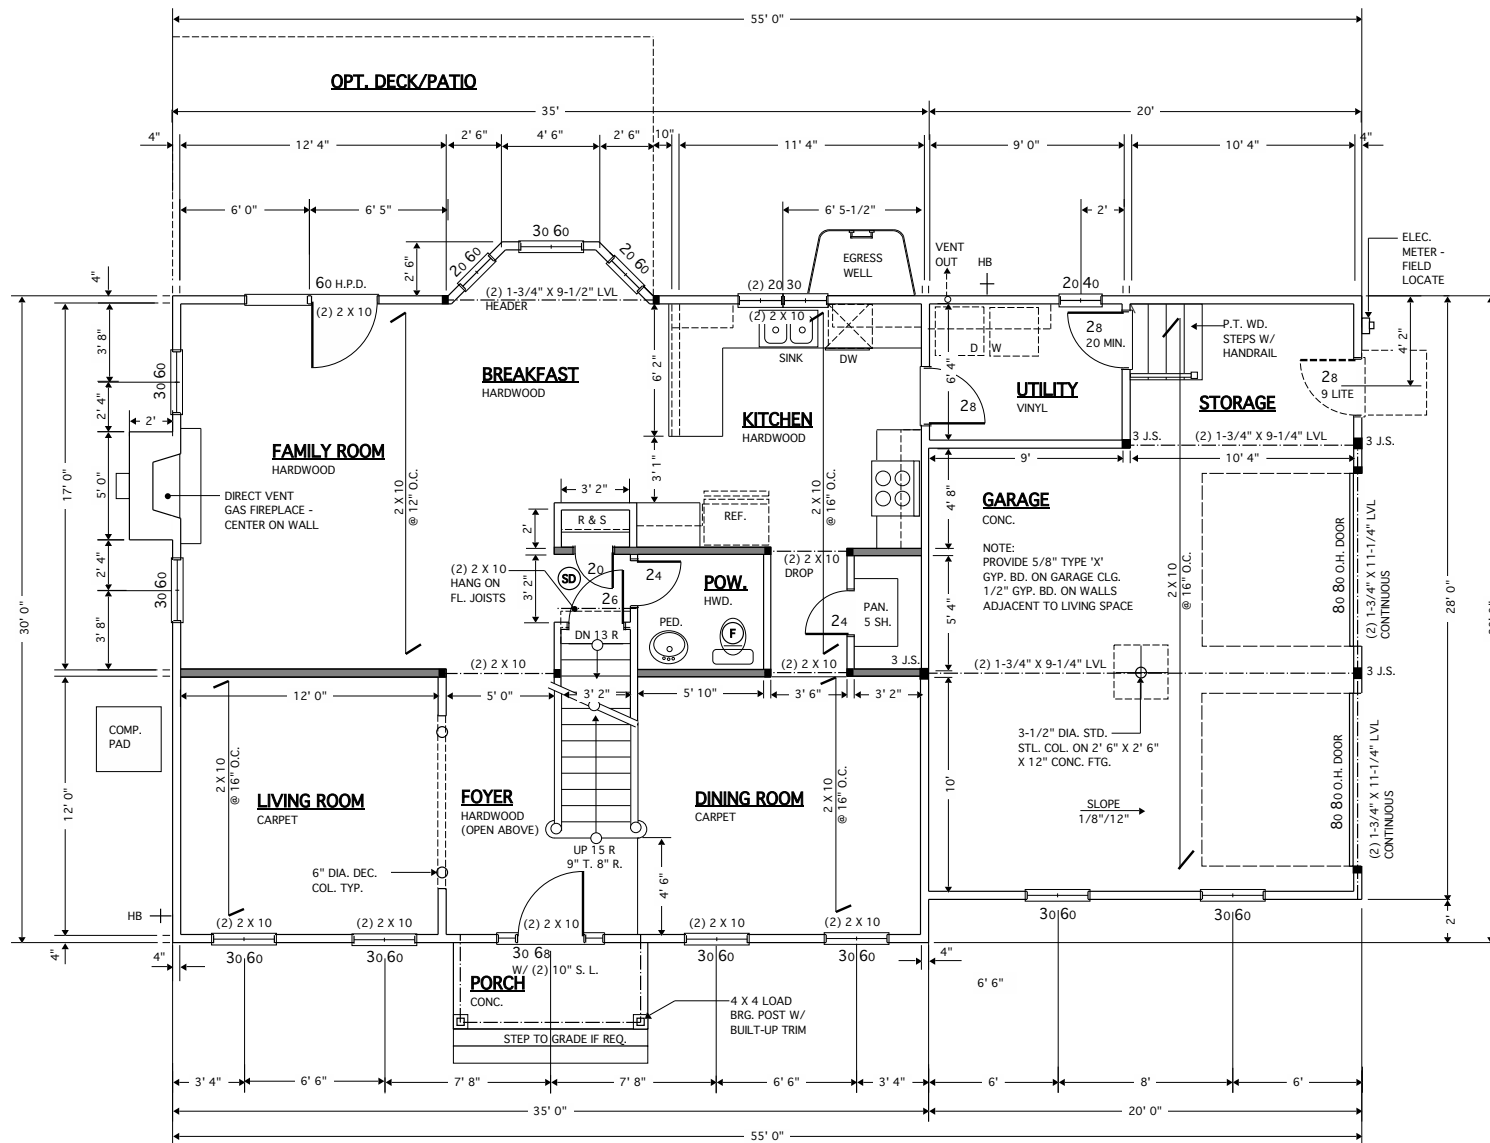

FIRST FLOOR PLAN

SCALE: 1/4"=1'-0"

REVISIONS	BY

JAMES WENTLING/ARCHITECT

100 S. BROAD STREET, SUITE 1524
PHILADELPHIA, PA 19110-1023
(215) 568-2551 (888) 675-5318 FAX
email - info@wentlinghouseplans.com



THE FAIRFIELD B MODEL

Client Address
City, State


DRAWN	DN
CHECKED	JW
DATE	09-20-11
SCALE	AS NOTED
JOB NO.	26-01 B
SHEET	3

FLOOR PLAN NOTES




1. ALL GLAZING SHALL MEET THE REQUIREMENTS OF **C.R.C. 308**. SAFETY GLAZING SHALL BE PROVIDED IN ALL OF THE FOLLOWING LOCATIONS:
- GLAZING IN DOORS SHALL BE CONSIDERED A HAZARDOUS LOCATION EXCEPT GLAZING PANELS THROUGH WITH A 3 INCH DIAMETER SPHERE IS UNABLE TO PASS AND DECORATIVE GLAZING.
- GLAZING IN WALLS, ENCLOSURES, OR FENCES FACING HOT TUBS, SPAS, WHIRLPOOLS, SAUNAS, STEAM ROOMS, BATHTUBS, SHOWERS AND INDOOR OR OUTDOOR SWIMMING POOLS WHERE THE BOTTOM EXPOSED EDGE OF THE GLAZING IS LESS THAN 60 INCHES MEASURED VERTICALLY ABOVE ANY STANDING OR WALKING SURFACE SHALL BE CONSIDERED A HAZARDOUS LOCATION. THIS SHALL APPLY TO SINGLE GLAZING AND ALL PANES IN MULTIPLE GLAZING.
- GLAZING IN AN INDIVIDUAL FIXED OR OPERABLE PANEL ADJACENT TO A DOOR WHERE THE BOTTOM EDGE OF THE GLAZING IS LESS THAN 60 INCHES ABOVE THE FLOOR OR WALKING SURFACE AND WHERE THE GLAZING IS WITHIN 24 INCHES OF EITHER SIDE OF THE DOOR IN THE PLANE OF THE DOOR IN A CLOSED POSITION OR WHERE THE GLAZING IS ON A WALL PERPENDICULAR TO THE PLANE OF THE DOOR IN A CLOSED POSITION AND WITHIN 24 INCHES OF THE HINGE SIDE OF AN IN-SWINGING DOOR.
- GLAZING WHERE THE BOTTOM EXPOSED EDGE OF THE GLAZING IS LESS THAN 36 INCHES ABOVE THE PLANE OF THE ADJACENT WALKING SURFACE OF STAIRWAYS, LANDINGS BETWEEN FLIGHTS OF STAIRS AND RAMPS SHALL BE CONSIDERED A HAZARDOUS LOCATION.
2. CAULK ALL DOORS, WINDOWS, JOINTS AND AREAS REQUIRED TO PROVIDE A WEATHERPROOF SEAL.
3. DRYWALL NAILING SHALL BE IN ACCORDANCE WITH C.B.C. REQUIREMENTS FOR THE TYPES AND THICKNESSES BEING USED UNLESS OTHERWISE NOTED.
4. NO WATER CLOSET OR BIDET SHALL BE SET CLOSER THAN 15 INCHES FROM ITS CENTER TO A SIDE WALL OR OBSTRUCTION OR CLOSER THAN 30" CENTER TO CENTER TO A SIMILAR FIXTURE. THE CLEAR SPACE IN FRONT OF A WATER CLOSET, LAVATORY, OR BIDET SHALL BE NOT LESS THAN 24 INCHES. **C.P.C. 402.5**
5. BATHTUB AND SHOWER FLOORS AND WALLS ABOVE BATHTUBS WITH INSTALLED SHOWER HEADS AND IN SHOWER COMPARTMENTS SHALL BE FINISHED WITH A NONABSORBENT SURFACE. SUCH WALL SURFACES SHALL EXTEND TO A HEIGHT OF NOT LESS THAN 6 FEET ABOVE THE FLOOR. **C.R.C. 307.2**
6. WINDOW/FALL PROTECTION SHALL BE PROVIDED IN ACCORDANCE WITH **C.R.C. 312.2.1-312.2.2**
7. EGRESS WINDOW IN BEDROOM TO PROVIDE 5.7 SQUARE FEET OF CLEAR OPENING AND A MINIMUM CLEAR NET OPENING HEIGHT OF 24" AND WIDTH OF 20" **PER C.R.C. 310.2.1**

PLUMBING NOTES

1. ALL PLUMBING FOR THIS PROJECT IS NEW
2. SHOWERS AND TUB-SHOWER COMBINATIONS SHALL BE PROVIDED WITH INDIVIDUAL CONTROL VALVES OF THE PRESSURE BALANCE, THERMOSTATIC, OR COMBINATION PRESSURE BALANCE/THERMOSTATIC MIXING VALVE TYPE THAT PROVIDE SCALD AND THERMAL SHOCK PROTECTION FOR THE RATED FLOW RATE OF THE INSTALLED SHOWERHEAD. THESE VALVES SHALL BE INSTALLED AT THE POINT OF USE AND IN ACCORDANCE WITH ASSE 1016, OR ASME A112.1016/CSA B125.16 OR ASME A112.18.1/CSA B125.1. HANDLE POSITION STOPS SHALL BE PROVIDED ON SUCH VALVES AND SHALL BE ADJUSTED PER THE MANUFACTURER'S INSTRUCTIONS TO DELIVER A MAXIMUM MIXED WATER SETTING OF 120°F (49°C). **C.P.C. 408.3**
3. CONTROL VALVES AND SHOWERHEADS SHALL BE LOCATED ON THE SIDEWALL OF SHOWER COMPARTMENTS OR OTHERWISE ARRANGED SO THAT THE SHOWERHEAD DOES NOT DIRECTLY AT THE ENTRANCE TO THE COMPARTMENT SO THAT THE BATHER CAN ADJUST THE VALVES BEFORE STEPPING INTO THE SHOWER SPRAY. **C.P.C. 408.9**
4. WATER HEATERS INSTALLED ON THIS PROJECT SHALL BE ANCHORED OR STRAPPED TO RESIST HORIZONTAL DISPLACEMENT DUE TO EARTHQUAKE MOTION. STRAPPING SHALL BE AT POINTS WITHIN THE UPPER ONE-THIRD AND LOWER ONE-THIRD OF ITS VERTICAL DIMENSIONS. AT THE LOWER POINT, A MINIMUM DISTANCE OF 4 IN. SHALL BE MAINTAINED ABOVE THE CONTROLS WITH THE STRAPPING. **C.P.C. 507.2** THIS APPLIES TO ALL NEW AND EXISTING WATER HEATERS PER THE CALIFORNIA HEALTH AND SAFETY CODE SECTION 19211(a)
5. WHERE A WATER HEATER IS INSTALLED PIPING SHALL BE INSULATED AS REQUIRED IN. **C.E.C. 150(J) 2**
6. POTABLE WATER OUTLETS WITH HOSE ATTACHMENTS OTHER THAN WATER HEATER DRAINS, BOILER DRAINS, AND CLOTHES WASHER CONNECTIONS. SHALL BE PROTECTED BY A NON REMOVABLE HOSE-BIB-TYPE BACKFLOW PREVENTER, A NON REMOVABLE HOSE BIB TYPE VACUUM BREAKER, OR BY AN ATMOSPHERIC VACUUM BREAKER INSTALLED NOT LESS THAN 6 IN. ABOVE THE HIGHEST POINT OF USAGE LOCATED ON THE DISCHARGE SIDE OF THE LAST VALVE. **C.P.C. 603.5.7**
7. EACH PLUMBING VENT SHALL TERMINATE NOT LESS THAN 10 FEET FROM, OR NOT LESS THAN 3 FEET ABOVE, AN OPENABLE WINDOW, DOOR, OPENING, AIR INTAKE, OR VENT SHAFT, OR NOT LESS THAN 3 FEET FROM A LOT LINE, ALLEY AND STREET EXCEPTED. **C.P.C. 906.2**

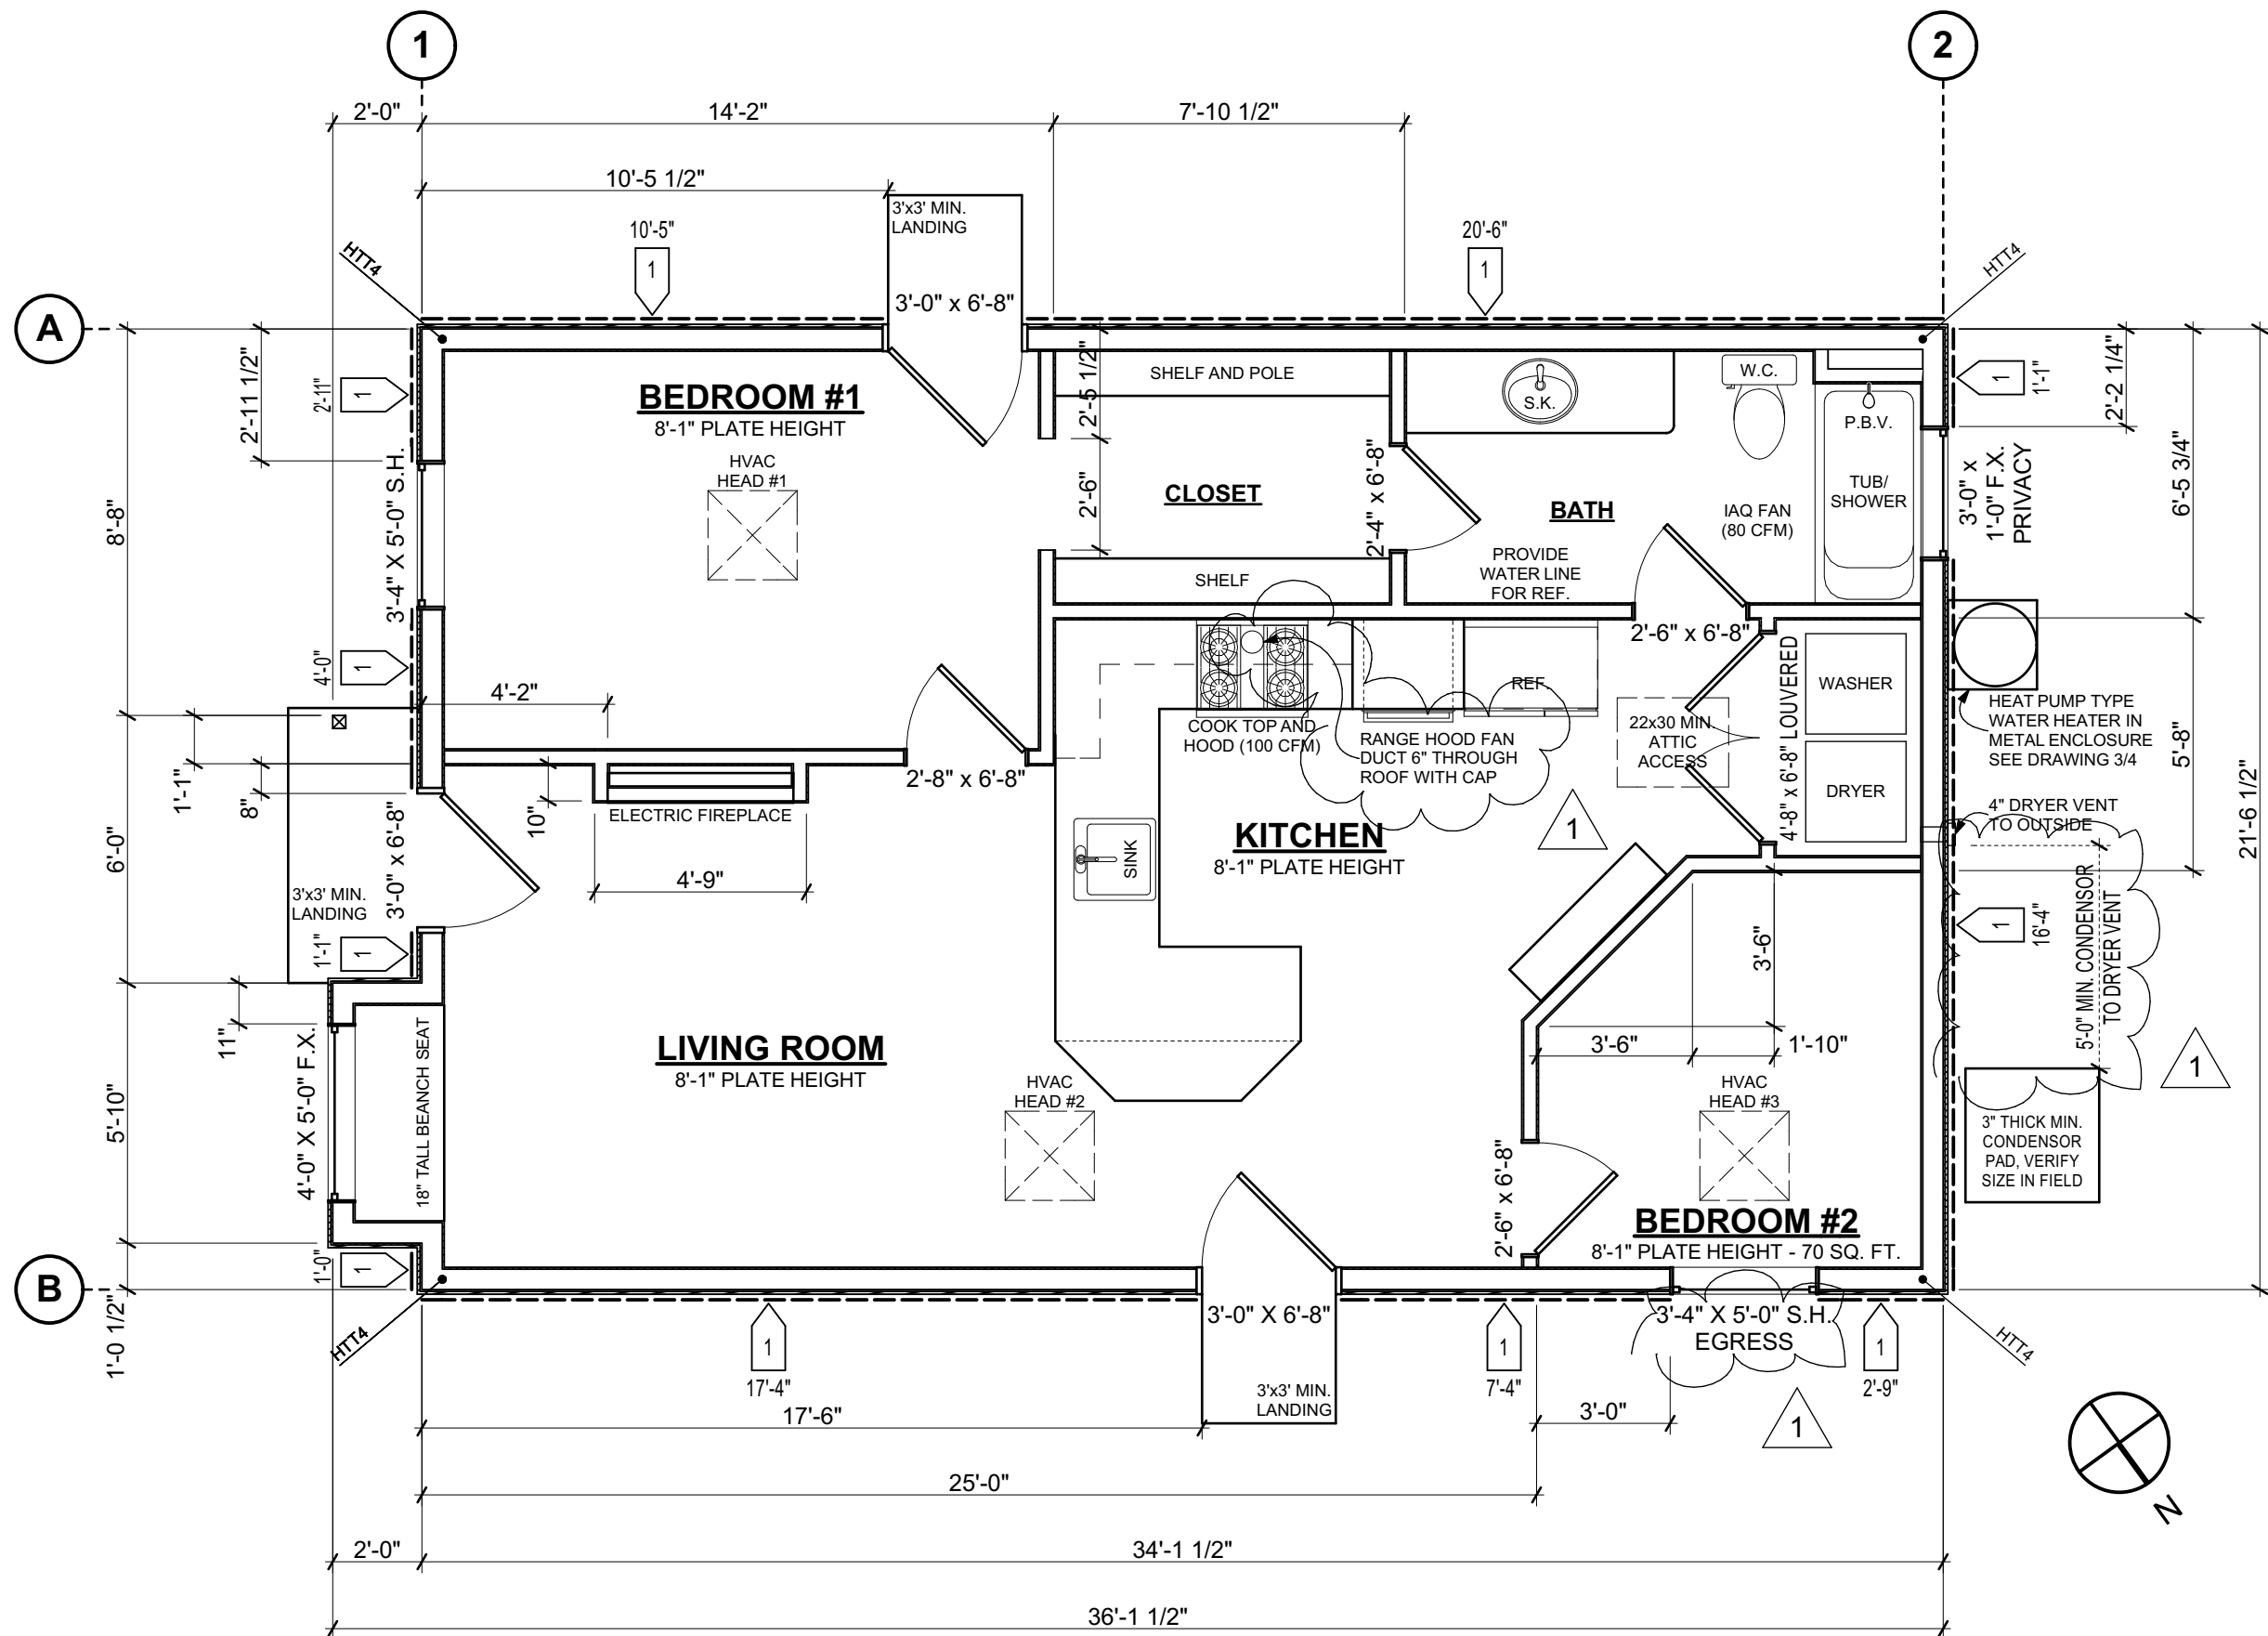

5 FLOOR PLAN
SCALE: 1/4" = 1'-0"

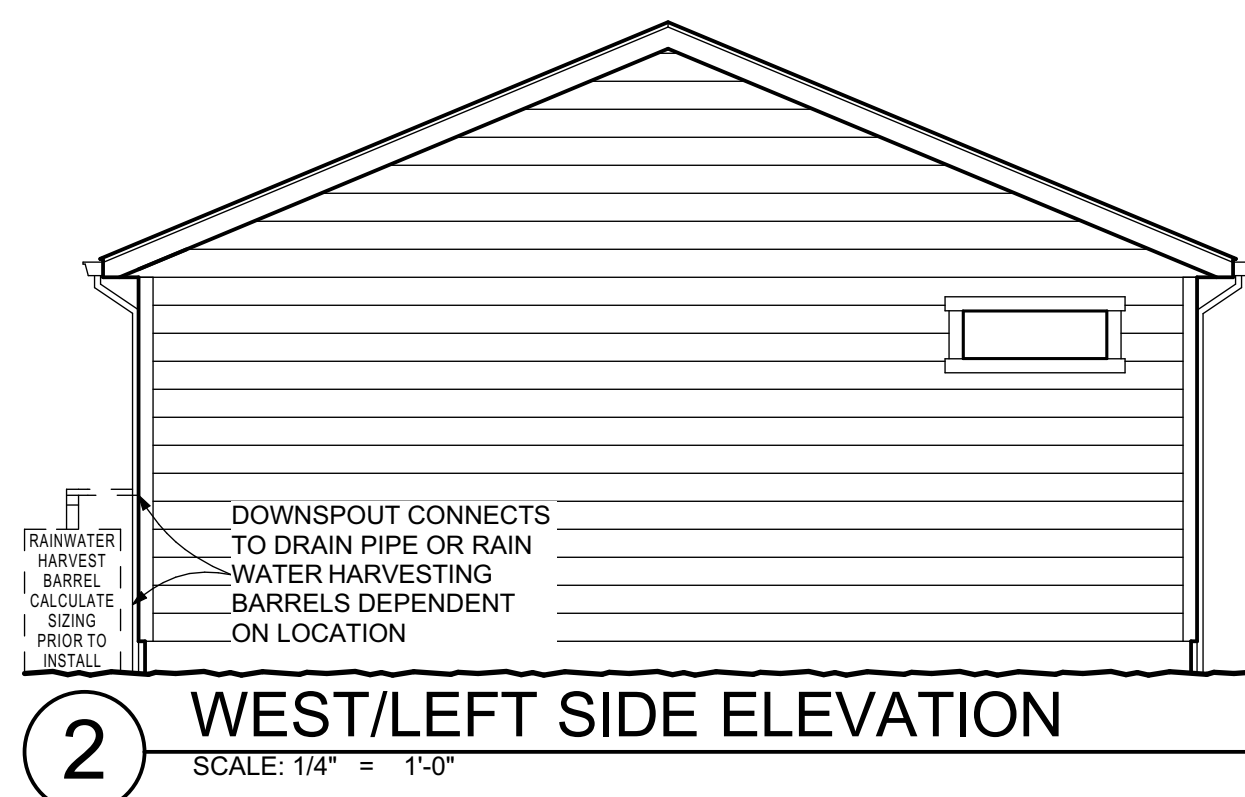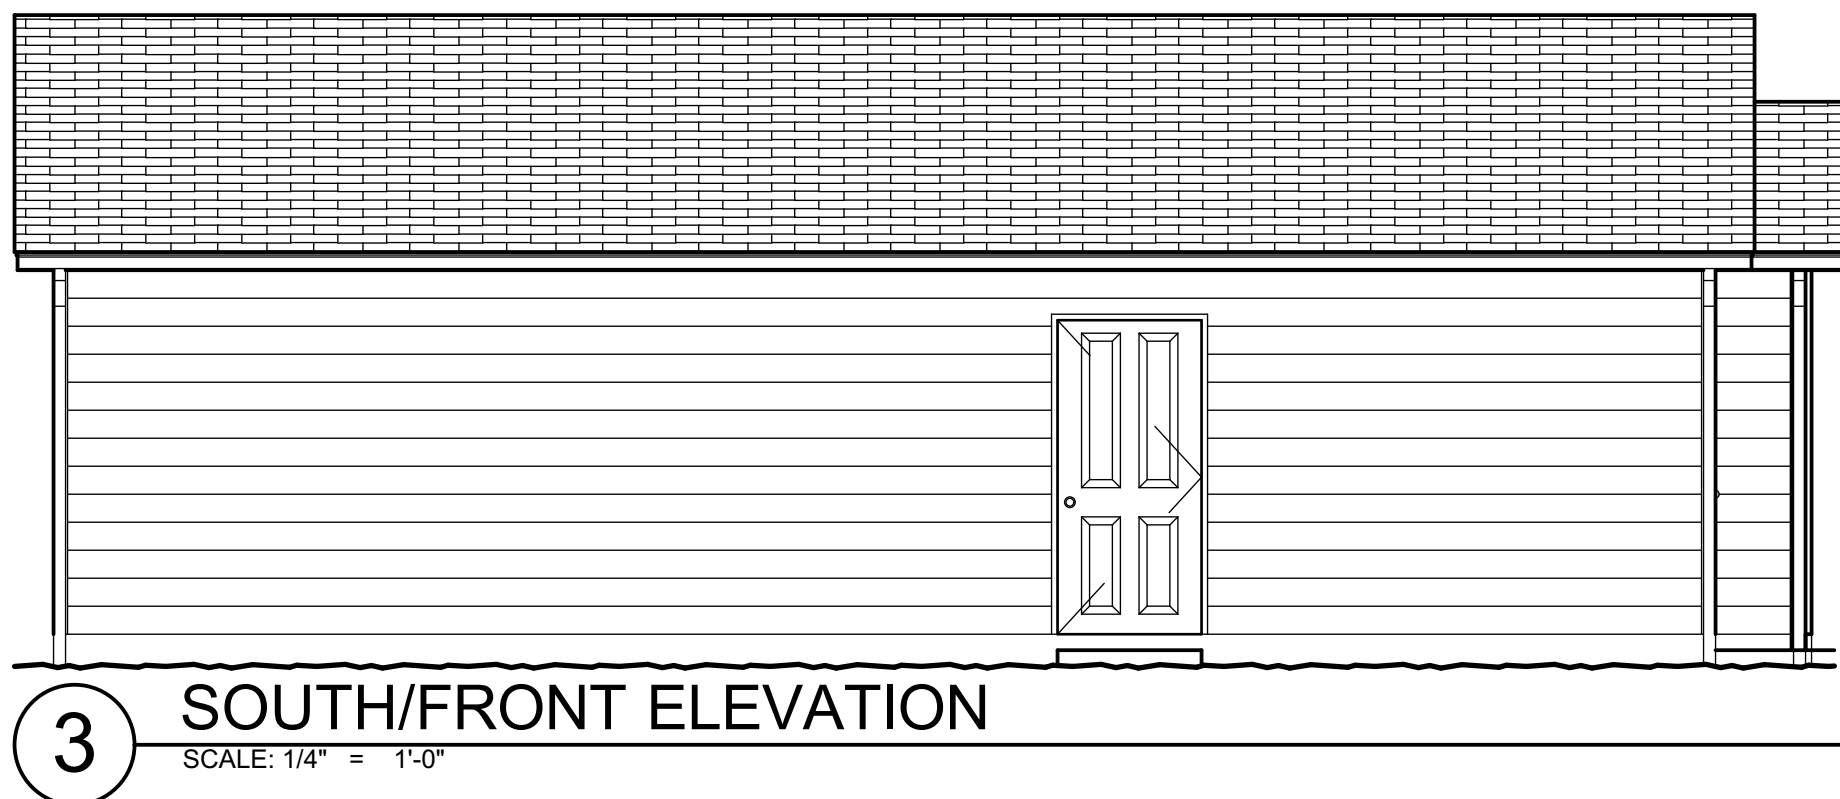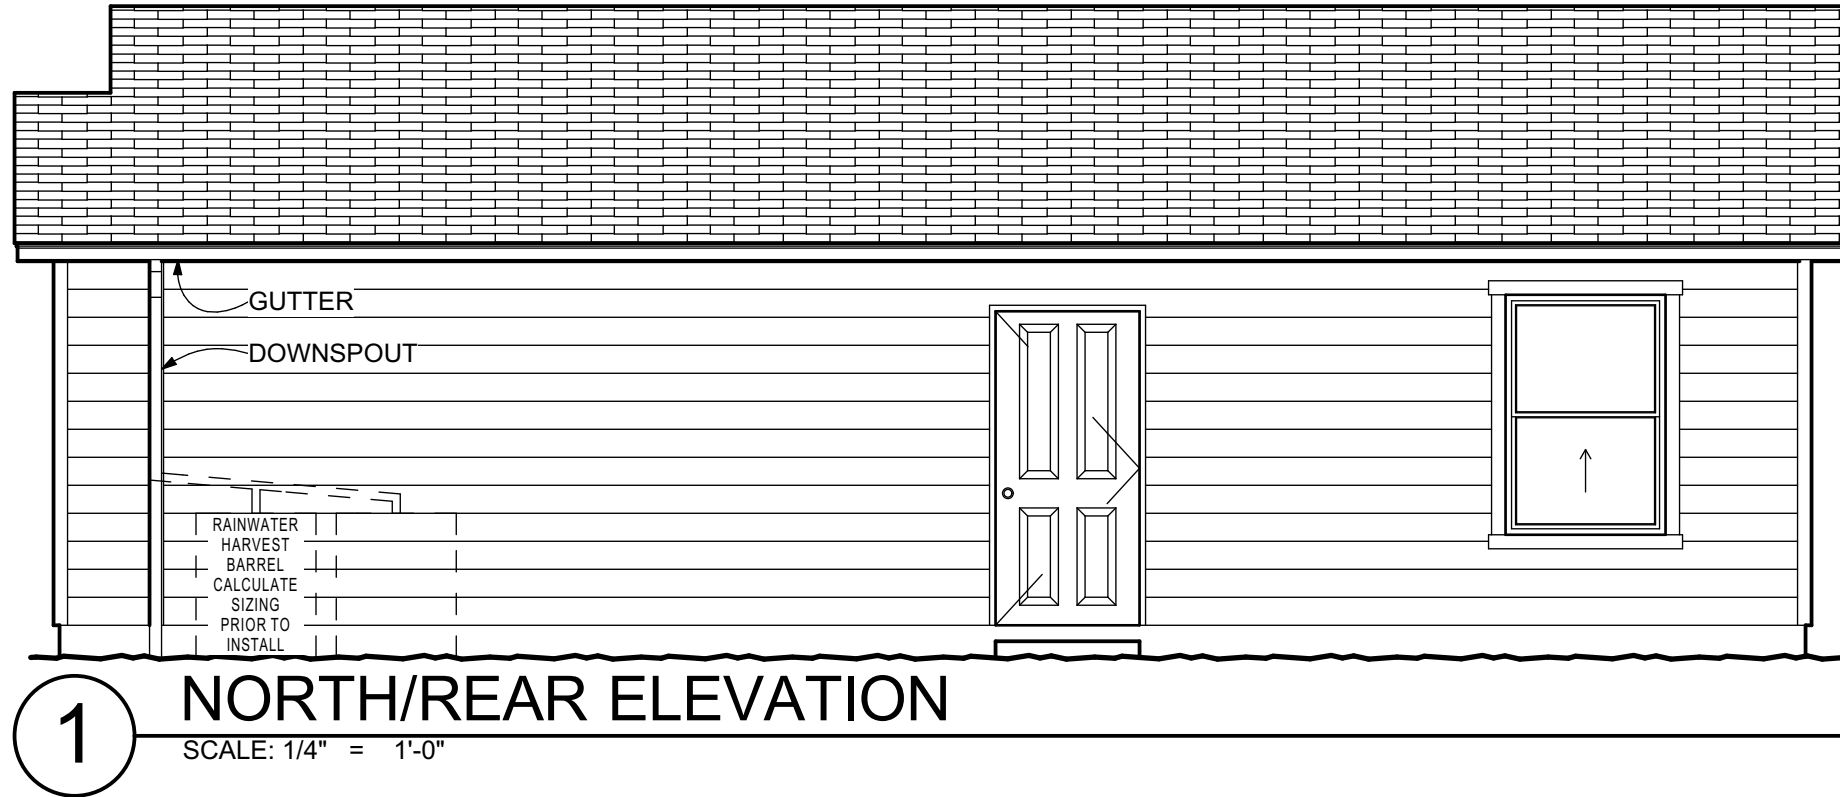

SHEAR WALL SCHEDULE

MARK	DESCRIPTION
1	15/32" C-C, C-D, OR OSB SHEATHING 8d COMMONS @ 6" O.C. AT ALL PANEL EDGES AND 12" O.C. IN THE FIELD. PLYWOOD SHALL BE ON ONE FACE WITH ALL EDGES BLOCKED. THE SILL PLATES SHALL BE ANCHORED WITH TWO 5/8"Ø A.B. MIN. PLACED AT 48" MAX. WITH 3" x 3" x 1/4" PLATE WASHERS AT FOUNDATION LEVEL FOR PLATES ANDCHORED TO FRAMING. SEE SHEAR WALL PANEL NOTES.
2	15/32" C-C, C-D, OR OSB SHEATHING 8d COMMONS @ 4" O.C. AT ALL PANEL EDGES AND 12" O.C. IN THE FIELD. PLYWOOD SHALL BE ON ONE FACE WITH ALL EDGES BLOCKED. THE SILL PLATES SHALL BE ANCHORED WITH TWO 5/8"Ø A.B. MIN. PLACED AT 32" MAX. WITH 3" x 3" x 1/4" PLATE WASHERS AT FOUNDATION LEVEL FOR PLATES ANDCHORED TO FRAMING. SEE SHEAR WALL PANEL NOTES.
3	15/32" C-C, C-D, OR OSB SHEATHING 10d COMMONS @ 3" O.C. AT ALL PANEL EDGES AND 12" O.C. IN THE FIELD. PLYWOOD SHALL BE ON ONE FACE WITH ALL EDGES BLOCKED. THE SILL PLATES SHALL BE ANCHORED WITH TWO 5/8"Ø A.B. MIN. PLACED AT 24" MAX. WITH 3" x 3" x 1/4" PLATE WASHERS AT FOUNDATION LEVEL FOR PLATES ANDCHORED TO FRAMING. SEE SHEAR WALL PANEL NOTES.
4	15/32" C-C, C-D, OR OSB SHEATHING 10d COMMONS @ 2" O.C. STAGGERED AT ALL PANEL EDGES AND 12" O.C. IN THE FIELD. PLYWOOD SHALL BE ON ONE FACE WITH ALL EDGES BLOCKED DOUBLE 2x FRAMING AT ALL PANEL EDGES. THE SILL PLATES SHALL BE ANCHORED WITH TWO 5/8"Ø A.B. MIN. PLACED AT 18" MAX. WITH 3" x 3" x 1/4" PLATE WASHERS AT FOUNDATION LEVEL FOR PLATES ANDCHORED TO FRAMING. SEE SHEAR WALL PANEL NOTES.

SHEAR WALL NOTES:

- LENGTHS (L) SHOWN ARE MINIMUMS. THE CONTRACTOR IS RESPONSIBLE FOR MAKING ALL WALL LINES FLUSH.
- ANCHOR BOLTS SHALL HAVE 7" MIN. EMBEDMENT AND SHALL BE LOCATED NOT MORE THAN 12" OR CLOSER THAN 4" FROM THE SILL PLATE ENDS.
- No. 6x1-1/4" SCREWS MAY BE USED IN LIEU OF 5d COOLER NAILS.

FLOOR PLAN LEGEND

- 2x6 WALLS
- 2x4 WALLS

ABBREVIATIONS

- AT
DOUBLE
EXISTING
GARBAGE DISPOSAL
MINIMUM
ON CENTER
ORIENTED STRAND BOARD
OVERHANG
NEW
PRESSURE BALANCE VALVE
ROUGH OPENING
SINGLE HUNG
SINK
SLIDING WINDOW
TYPICAL
TANKLESS WATER HEATER
UNLESS OTHERWISE NOTED
WATER CLOSET
WITH
- @ DBL.
(E)
G.D.
MIN.
O.C.
O.S.B.
O.V.H.
(N)
P.B.V.
R.O.
S.H.
S.K.
S.L.
TYP
T.W.H.
U.O.N.
W.C.
W/

SHEAR WALL LEGEND

- INDICATES SHEAR WALL PANEL. SEE NOTES & SCHEDULE THIS SHEET
- INDICATES VERTICAL TIE DOWNSTRAP OR HOLDOWN. SEE SHEET 4 FOR DETAILS.

ВЕДОМОСТЬ ЭЛЕМЕНТОВ И ОБОРУДОВАНИЯ

Объект: жилой дом. Стадия П.

Поз.	Обозначение	Наименование	Тип/марка	Кол.	Масса, кг	Примечание
1	КМ-1	Колонна металлическая	200х200х8	8	86,0	По оси А
2	БМ-2	Балка перекрытия	30Б1	12	42,5	Между осями 1-4
3	ПСВ-101	Клапан предохранительный	Ду50 Ру40	2	12,5	Уставка 1,6 МПа
4	ПСВ-102	Клапан предохранительный	Ду80 Ру40	1	18,0	Уставка 1,6 МПа
5	ЗКЛ-210	Задвижка клиновая	Ду100 Ру25	4	42,0	Фланцевая
6	КШ-311	Кран шаровой	Ду50 Ру16	6	8,2	Ручной привод
7	КО-405	Клапан обратный	Ду80 Ру16	3	15,4	Поворотный
8	ДИ-501	Датчик расхода	Ду50	2	6,1	4-20 мА
9	ДД-502	Датчик давления	М20х1,5	2	3,8	HART
10	ТО-601	Теплообменник	кожухотрубный	1	210,0	Q=120 кВт
11	Н-701	Насос центробежный	Ду80	2	95,0	С резервом
12	Рез-801	Ёмкость накопительная	V=12 м3	1	450,0	Наружная установка

Итого позиций: 12

Пояснительная записка к комплекту рабочей документации

Стадия П. Демонстрационный комплект (базовый).

В составе комплекта приведены графические листы из типовых образцов (этажи и каркас), ведомость элементов и настоящая записка. Инженер проходит фильтры вкладок и отмечает просмотренные листы.

Критерии: во вкладке с графикой — скопированные листы образцов; в «Таблицы» — ведомость с ПСВ-101 и массой 210 кг; в «Текст» — эта записка.

Порядок работы: просмотреть графику, сверить позиции ведомости, при необходимости исправить текст, скачать Markdown.

Объём записки увеличен, чтобы классификатор отнёс лист к текстовому типу, а не к коротким выноскам графики.