


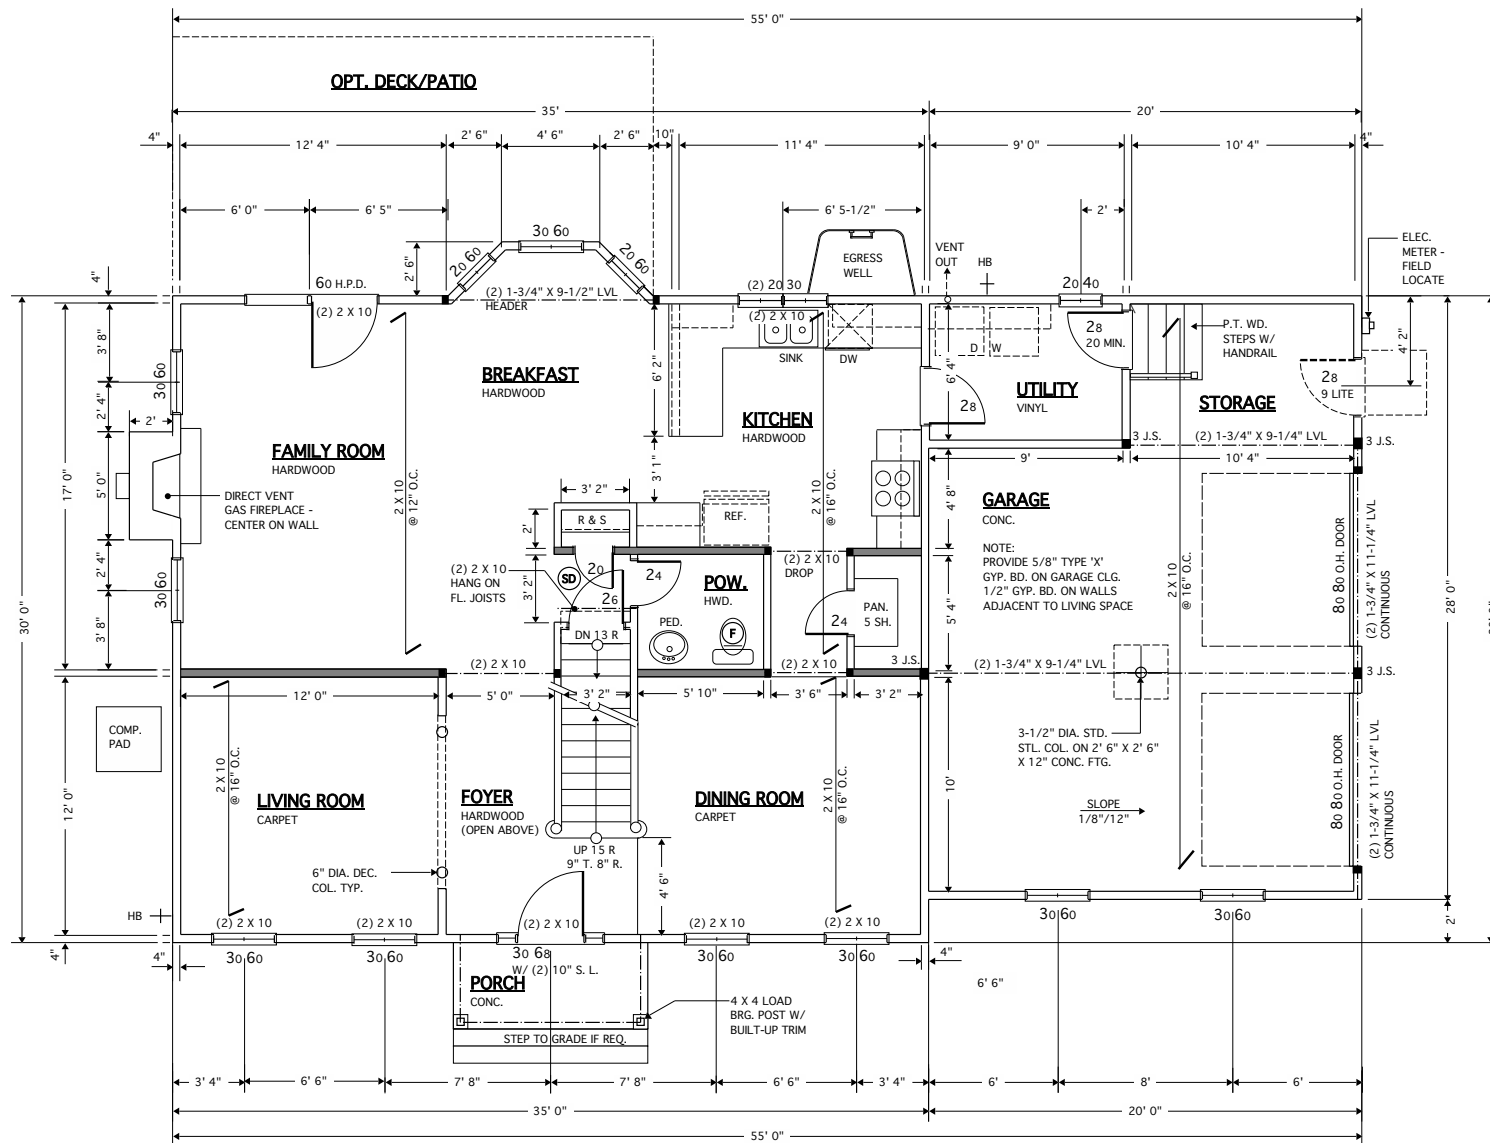

FIRST FLOOR PLAN

SCALE: 1/4"=1'-0"

REVISIONS	BY

JAMES WENTLING/ARCHITECT



100 S. BROAD STREET, SUITE 1524
PHILADELPHIA, PA 19110-1023
(215) 568-2551 (888) 675-5318 FAX
email - info@wentlinghouseplans.com



THE FAIRFIELD B MODEL

Client Address
City, State

DRAWN	DN
CHECKED	JW
DATE	09-20-11
SCALE	AS NOTED
JOB NO.	26-01 B
SHEET	3

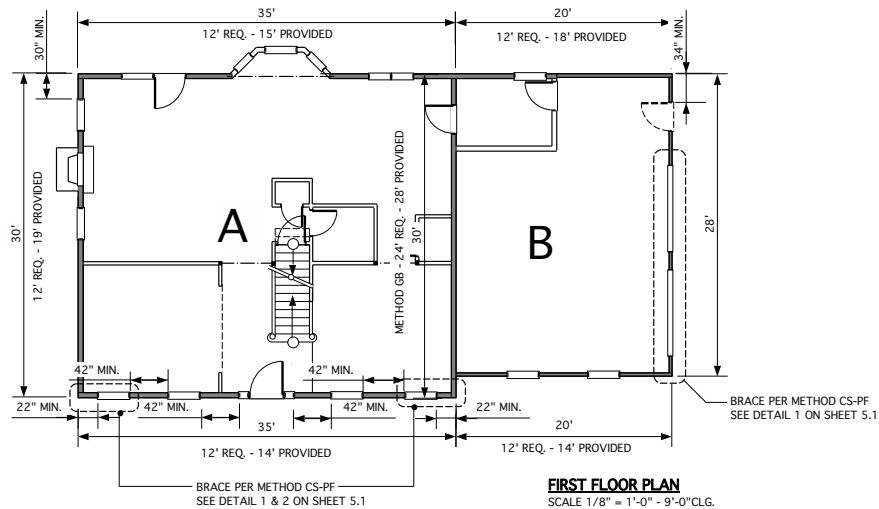
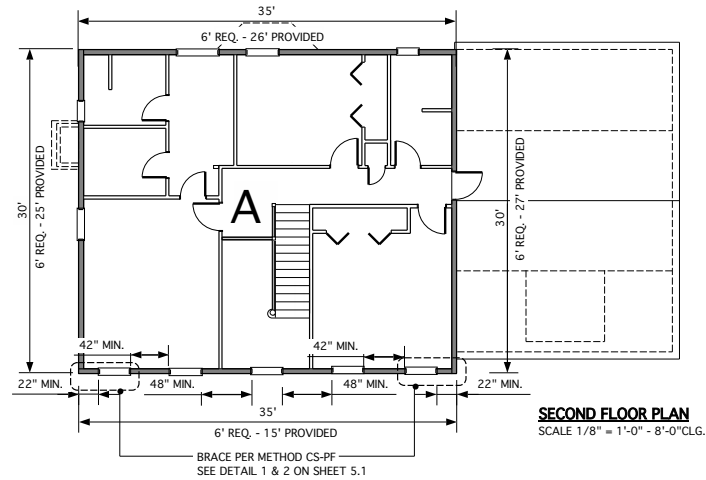


NOTE: ALL EXTERIOR WALLS ARE TO BE CONTINUOUSLY SHEATHED WITH 7/16" WOOD STRUCTURAL PANELS AND NAILED W/ 8d COMMON NAILS @ 6" O.C. AT EDGE, 12" O.C. AT FIELD PER METHOD 3, INTERNATIONAL RESIDENTIAL CODE, 2006 ED., TABLE R602.10.1

WALL BRACED WALL LINES CALCULATIONS - CODE REFERENCE: 2009 IRC, SECTION 602.10.4 CONTINUOUS SHEATHING METHOD




TABLE R602.10.1.2 (1) 90 MPH OR LESS, METHOD CS AND GB WITH BRACED WALL LINE SPACING @ 40'

REVISIONS	BY
JAMES WENTLING/ARCHITECT 100 S. BROAD STREET, SUITE 1524 PHILADELPHIA, PA 19101-1023 (215) 568-2551 (888) 675-5318 FAX	
THE FAIRFIELD B MODEL Client Address City, State	
DRAWN	DN
CHECKED	JW
DATE	09-15-11
SCALE	AS NOTED
JOB NO.	26-01 B
SHEET	3.2

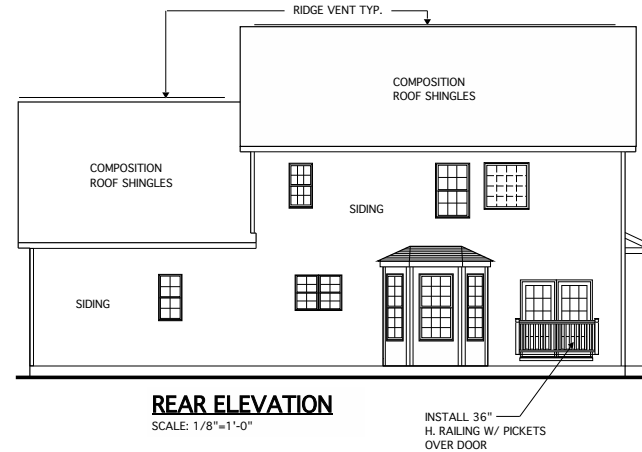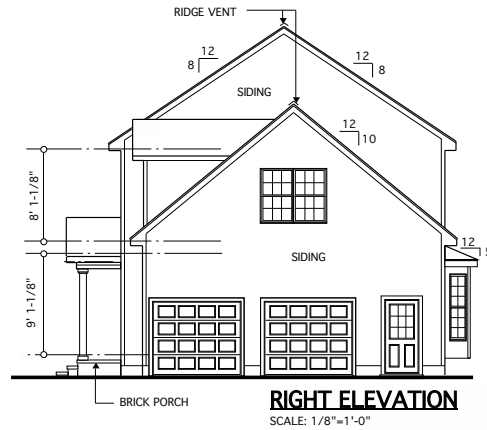

FRONT ELEVATION
SCALE: 1/4"=1'-0"

[illegible]

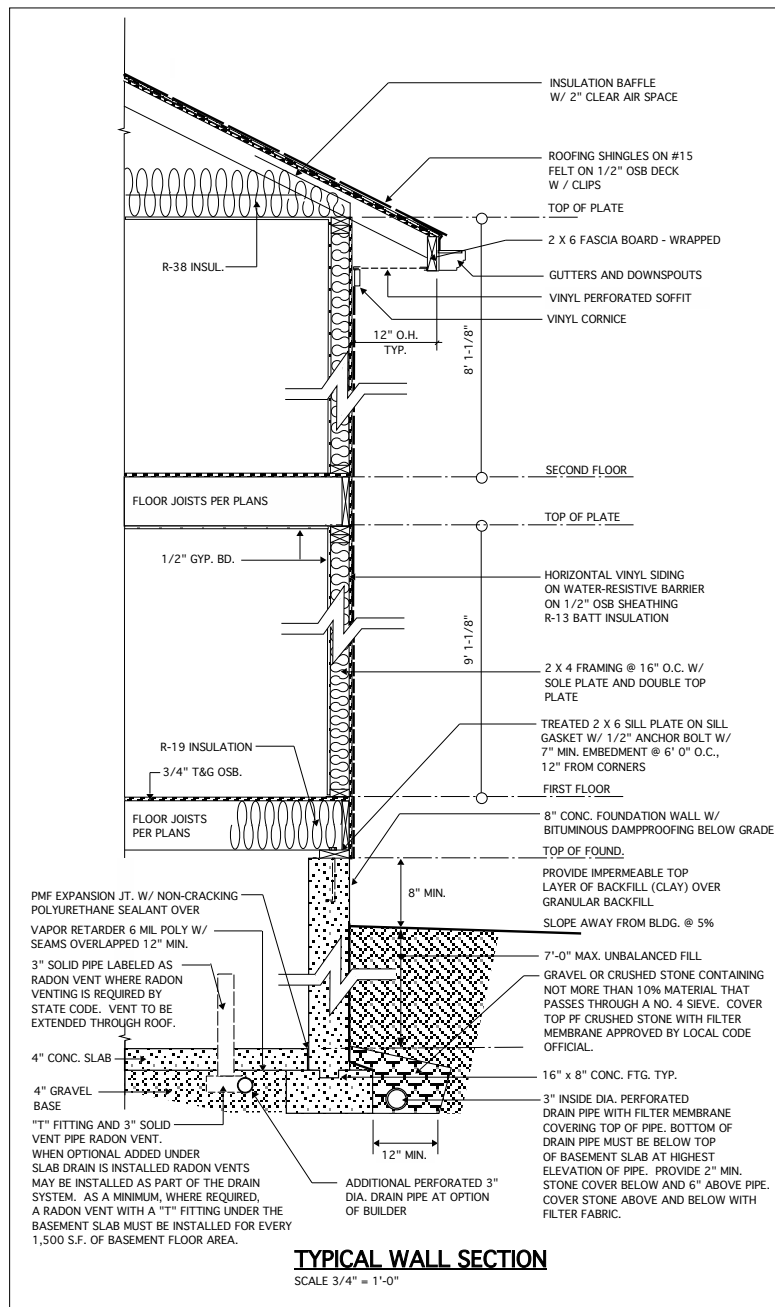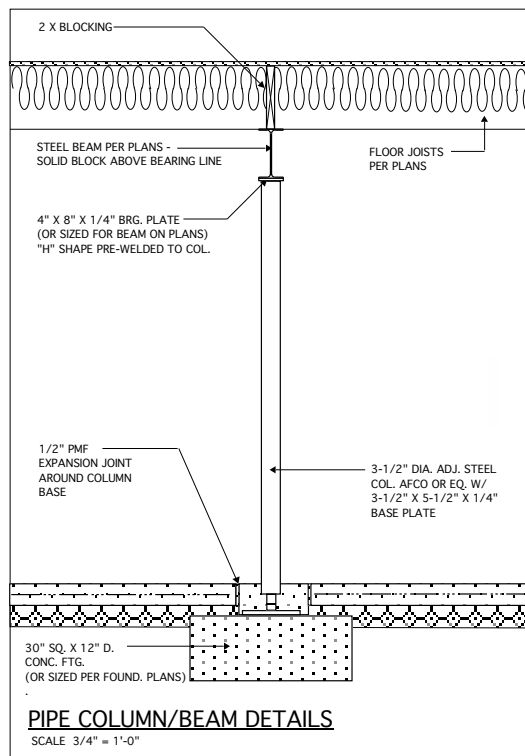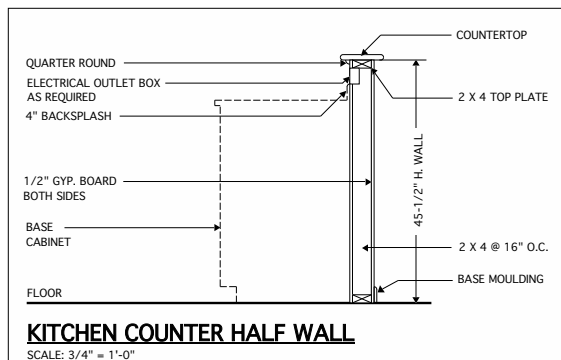[illegible]